


FOR ENGINEER REVIEW

OUTSIDE WALL

(EXTERIOR - EXISTING 12" CMU)

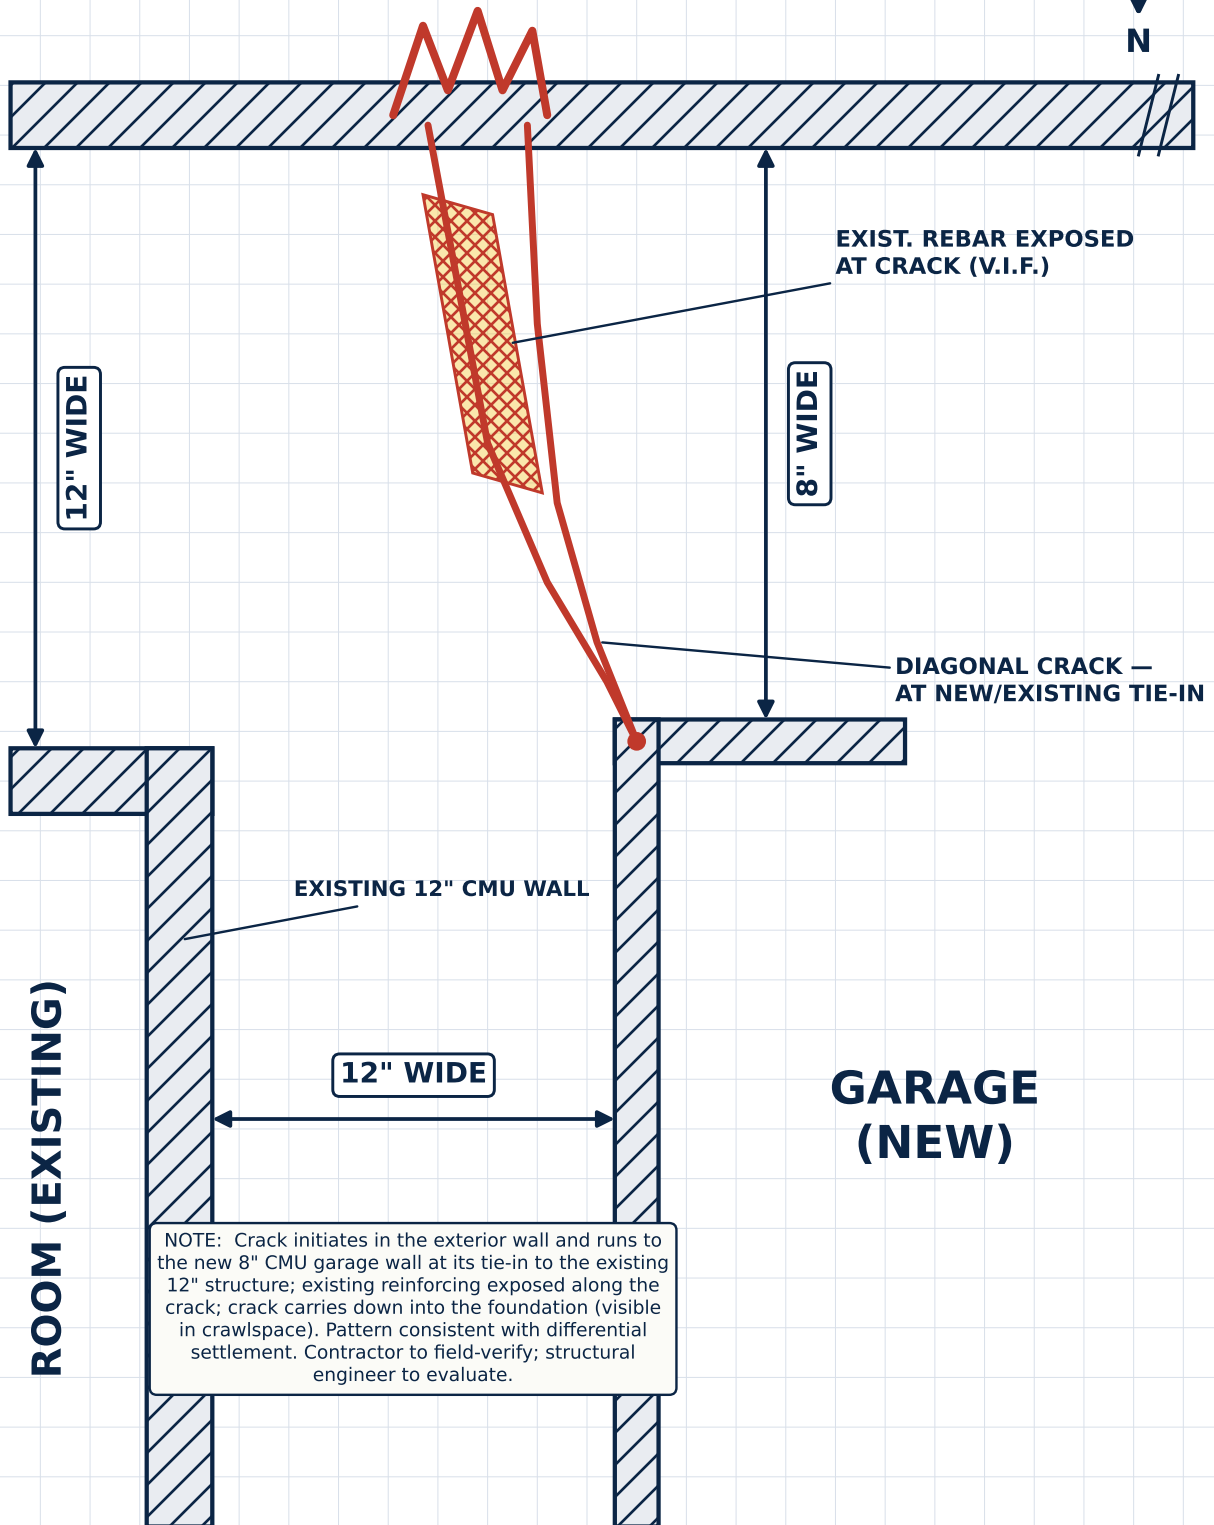

NOTE: Crack initiates in the exterior wall and runs to the new 8" CMU garage wall at its tie-in to the existing 12" structure; existing reinforcing exposed along the crack; crack carries down into the foundation (visible in crawlspace). Pattern consistent with differential settlement. Contractor to field-verify; structural engineer to evaluate.

LA GALA CONSTRUCTION

STRUCTURAL EXHIBIT

PROJECT: New Garage Addition to Existing Structure

SCALE: N.T.S.

DATE: 06/25/2026

DRAWING TITLE: CMU Wall — Crack at New Garage / Existing Tie-In (Plan)

LICENSE: CGC059211

SHEET: SK-1