


FOR ENGINEER REVIEW

OUTSIDE WALL

(EXTERIOR - EXISTING 12" CMU)

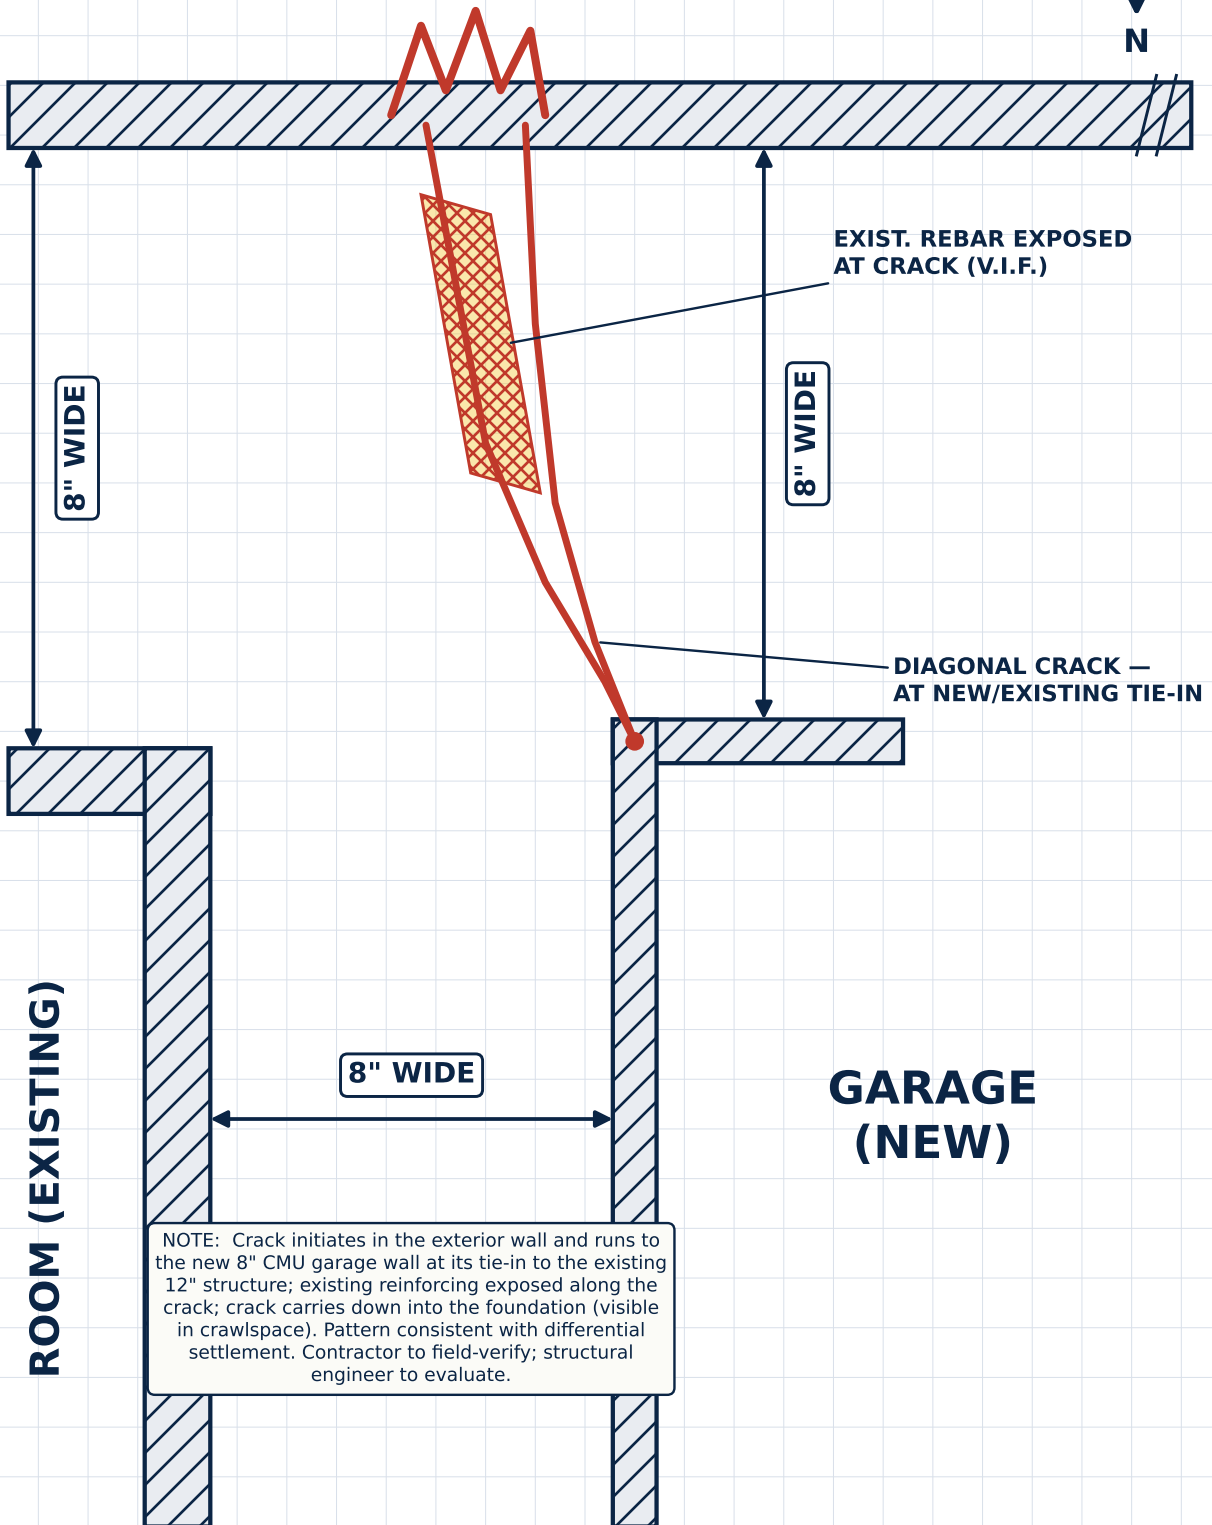

LA GALA CONSTRUCTION

STRUCTURAL EXHIBIT

PROJECT: New Garage Addition to Existing Structure

SCALE: N.T.S.

DATE: 06/25/2026

DRAWING TITLE: CMU Wall — Crack at New Garage / Existing Tie-In (Plan)

LICENSE: CGC059211

SHEET: SK-1